



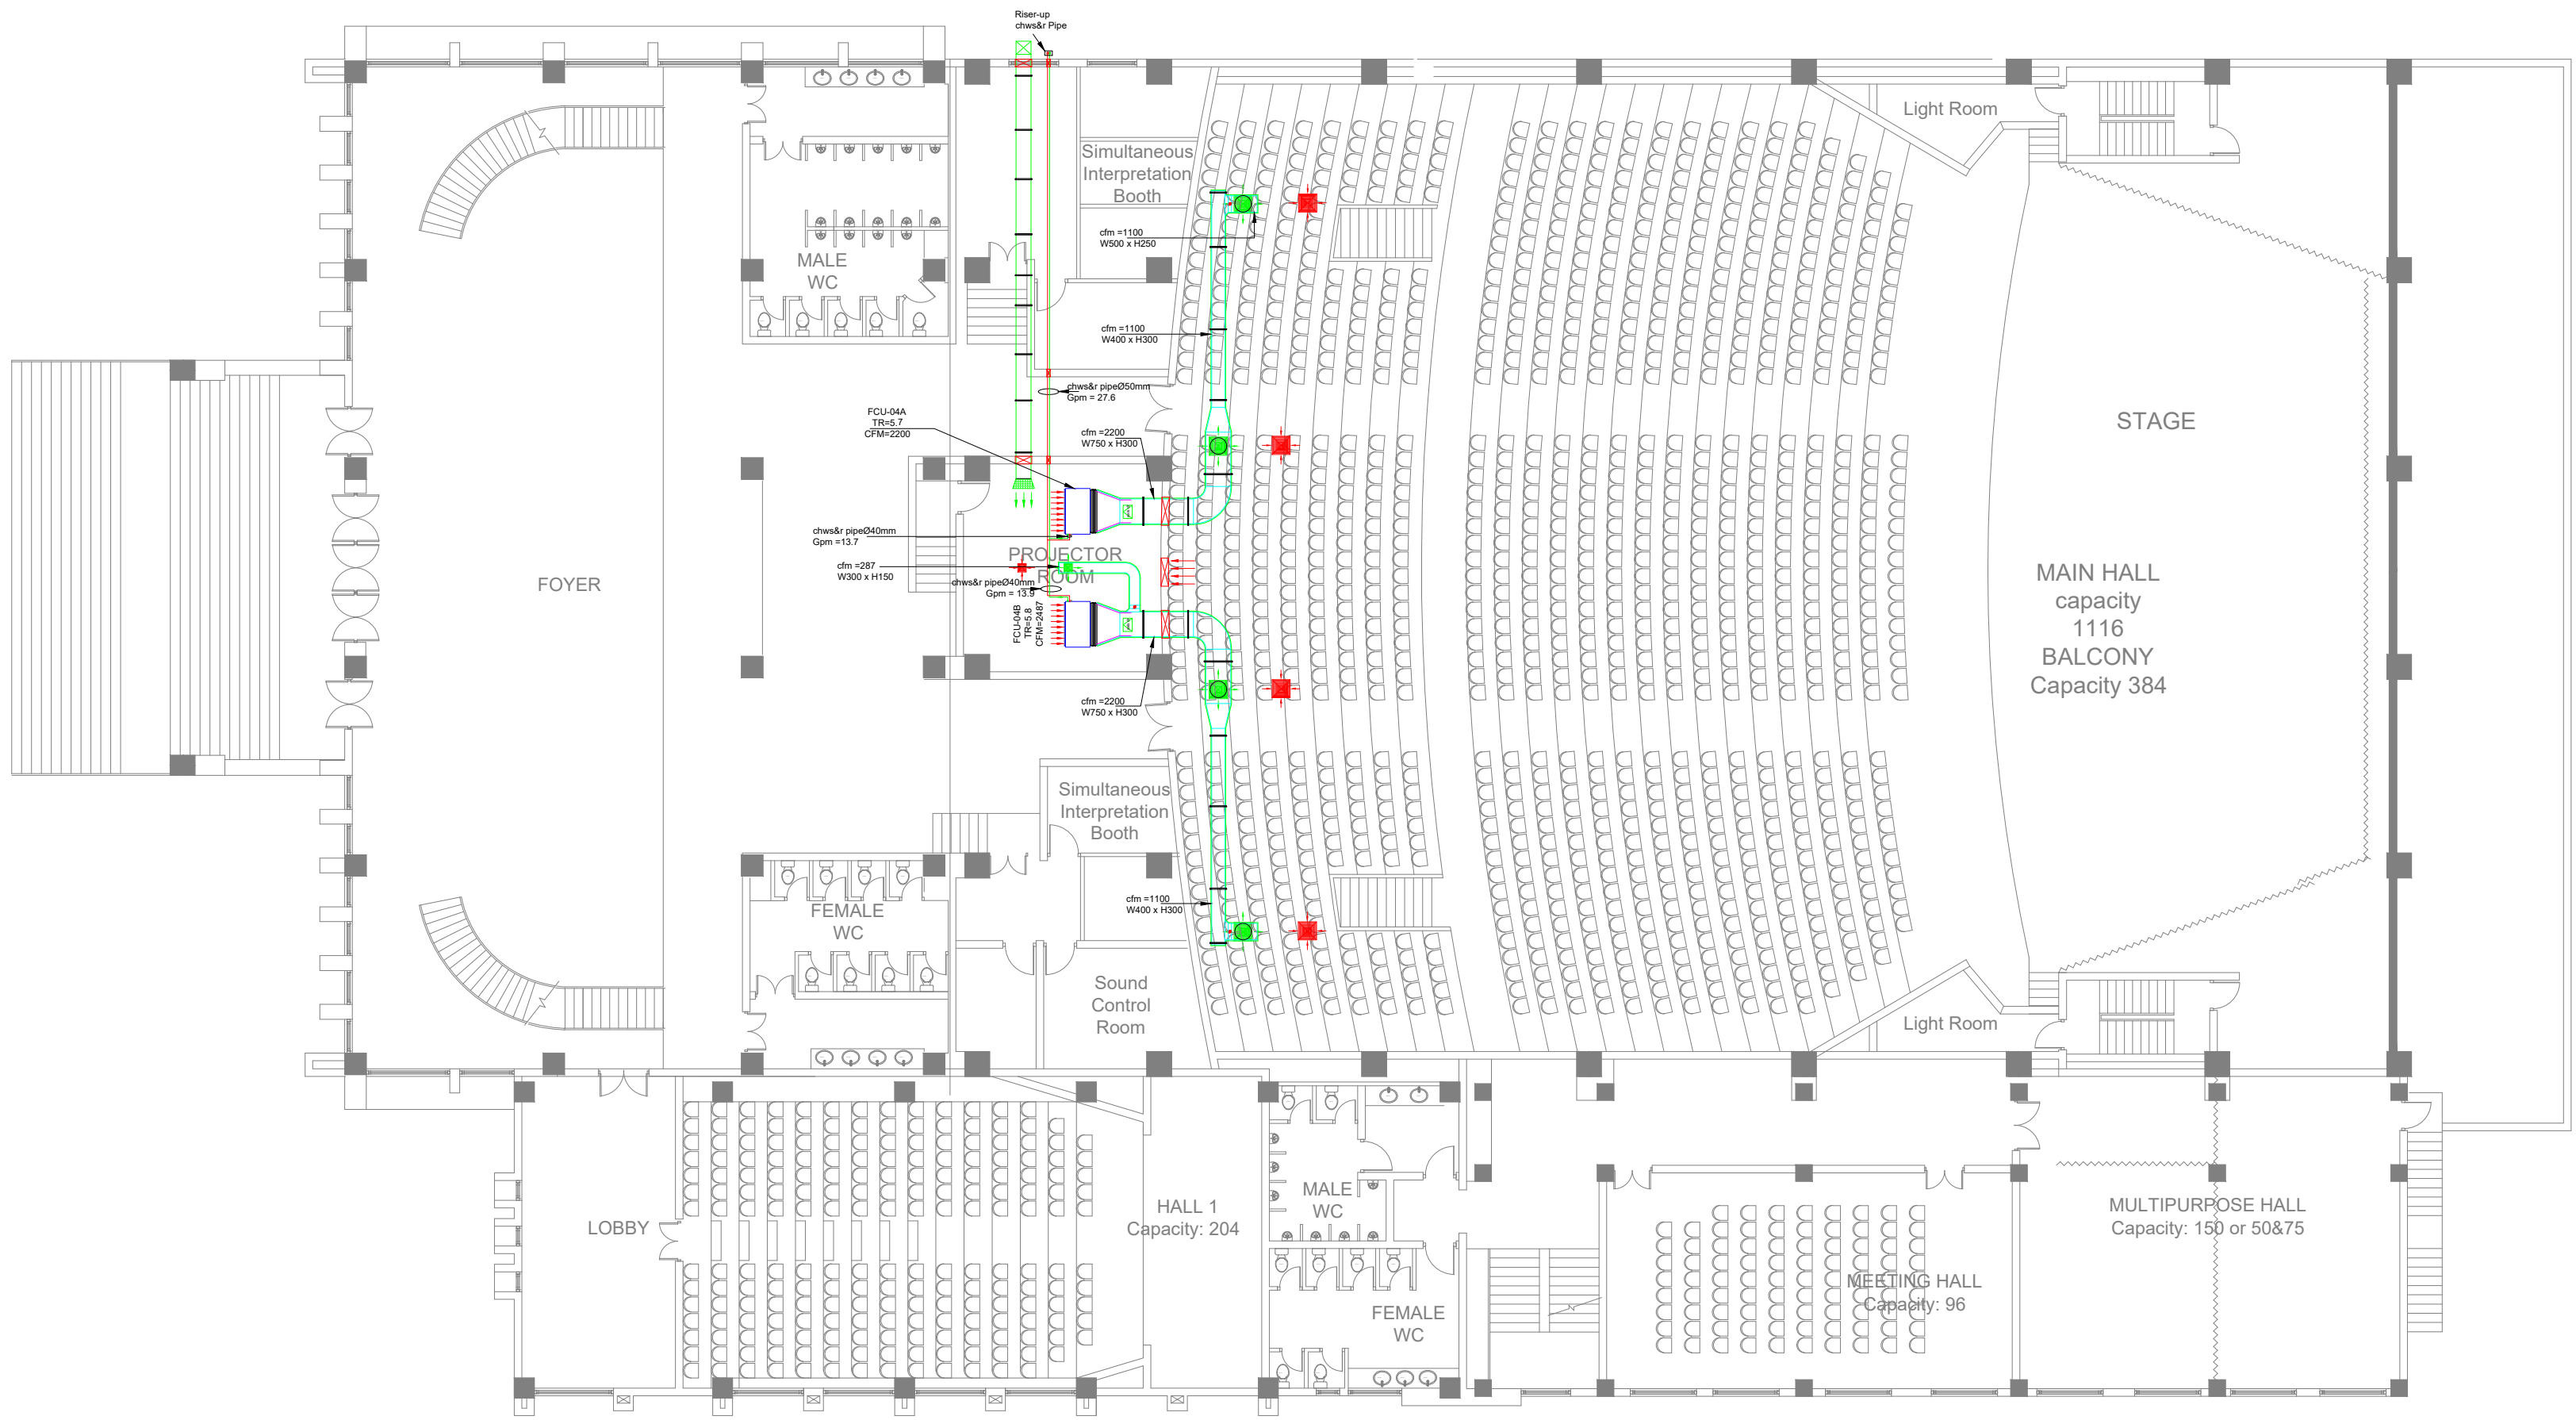

FIRST FLOOR PLAN
Area: 2473 Sq.m.
Scale= 1:250

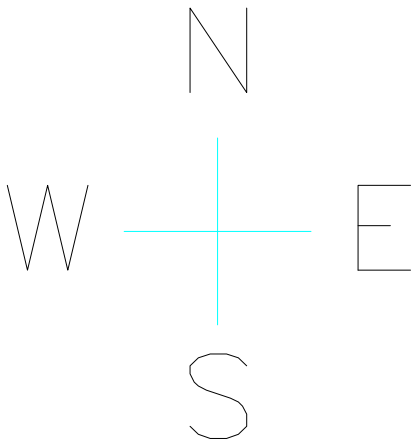

NOTE....
ALL DIMENSION ARE IN MM

SYMBOL	ABBREVIATION
	SUPPLY CEILING DIFFUSER(SCD)
	RETURN CEILING DIFFUSER(RCD)
	WALL OPENING
	FIRE DAMPER
	ACCESS DOOR
	SUPPORTS
	FLEXIBLE DUCT
	THERMOSTAT
	RETURN LINEAR GRILL
	SUPPLY LINEAR GRILL
	VARIABLE AIR VOLUME
	CIRCULAR VOLUME CONTROL DAMPER(VCD)
	INSULATION
	ACCOUSTIC LINING

CLIENT/PROJECT
AUDITORIUM
INDIA BANGLORE

M.E.P.
CONSULTANT

www.TaibaMEP.Com, tec_mep@yahoo.com, ali@taibamep.com
Ph : 040-64604442 / 9963759411 / 9848461870

Drg. title
FIRST FLOOR PLAN 02
HVAC DUCTING LAYOUT

SCALE	1:100	CHECKED BY ARSLAN A KHAN
DATE	11-12-2019	APPROVED MR. WASIM A K
DRAWN	AZAR PATEL	