



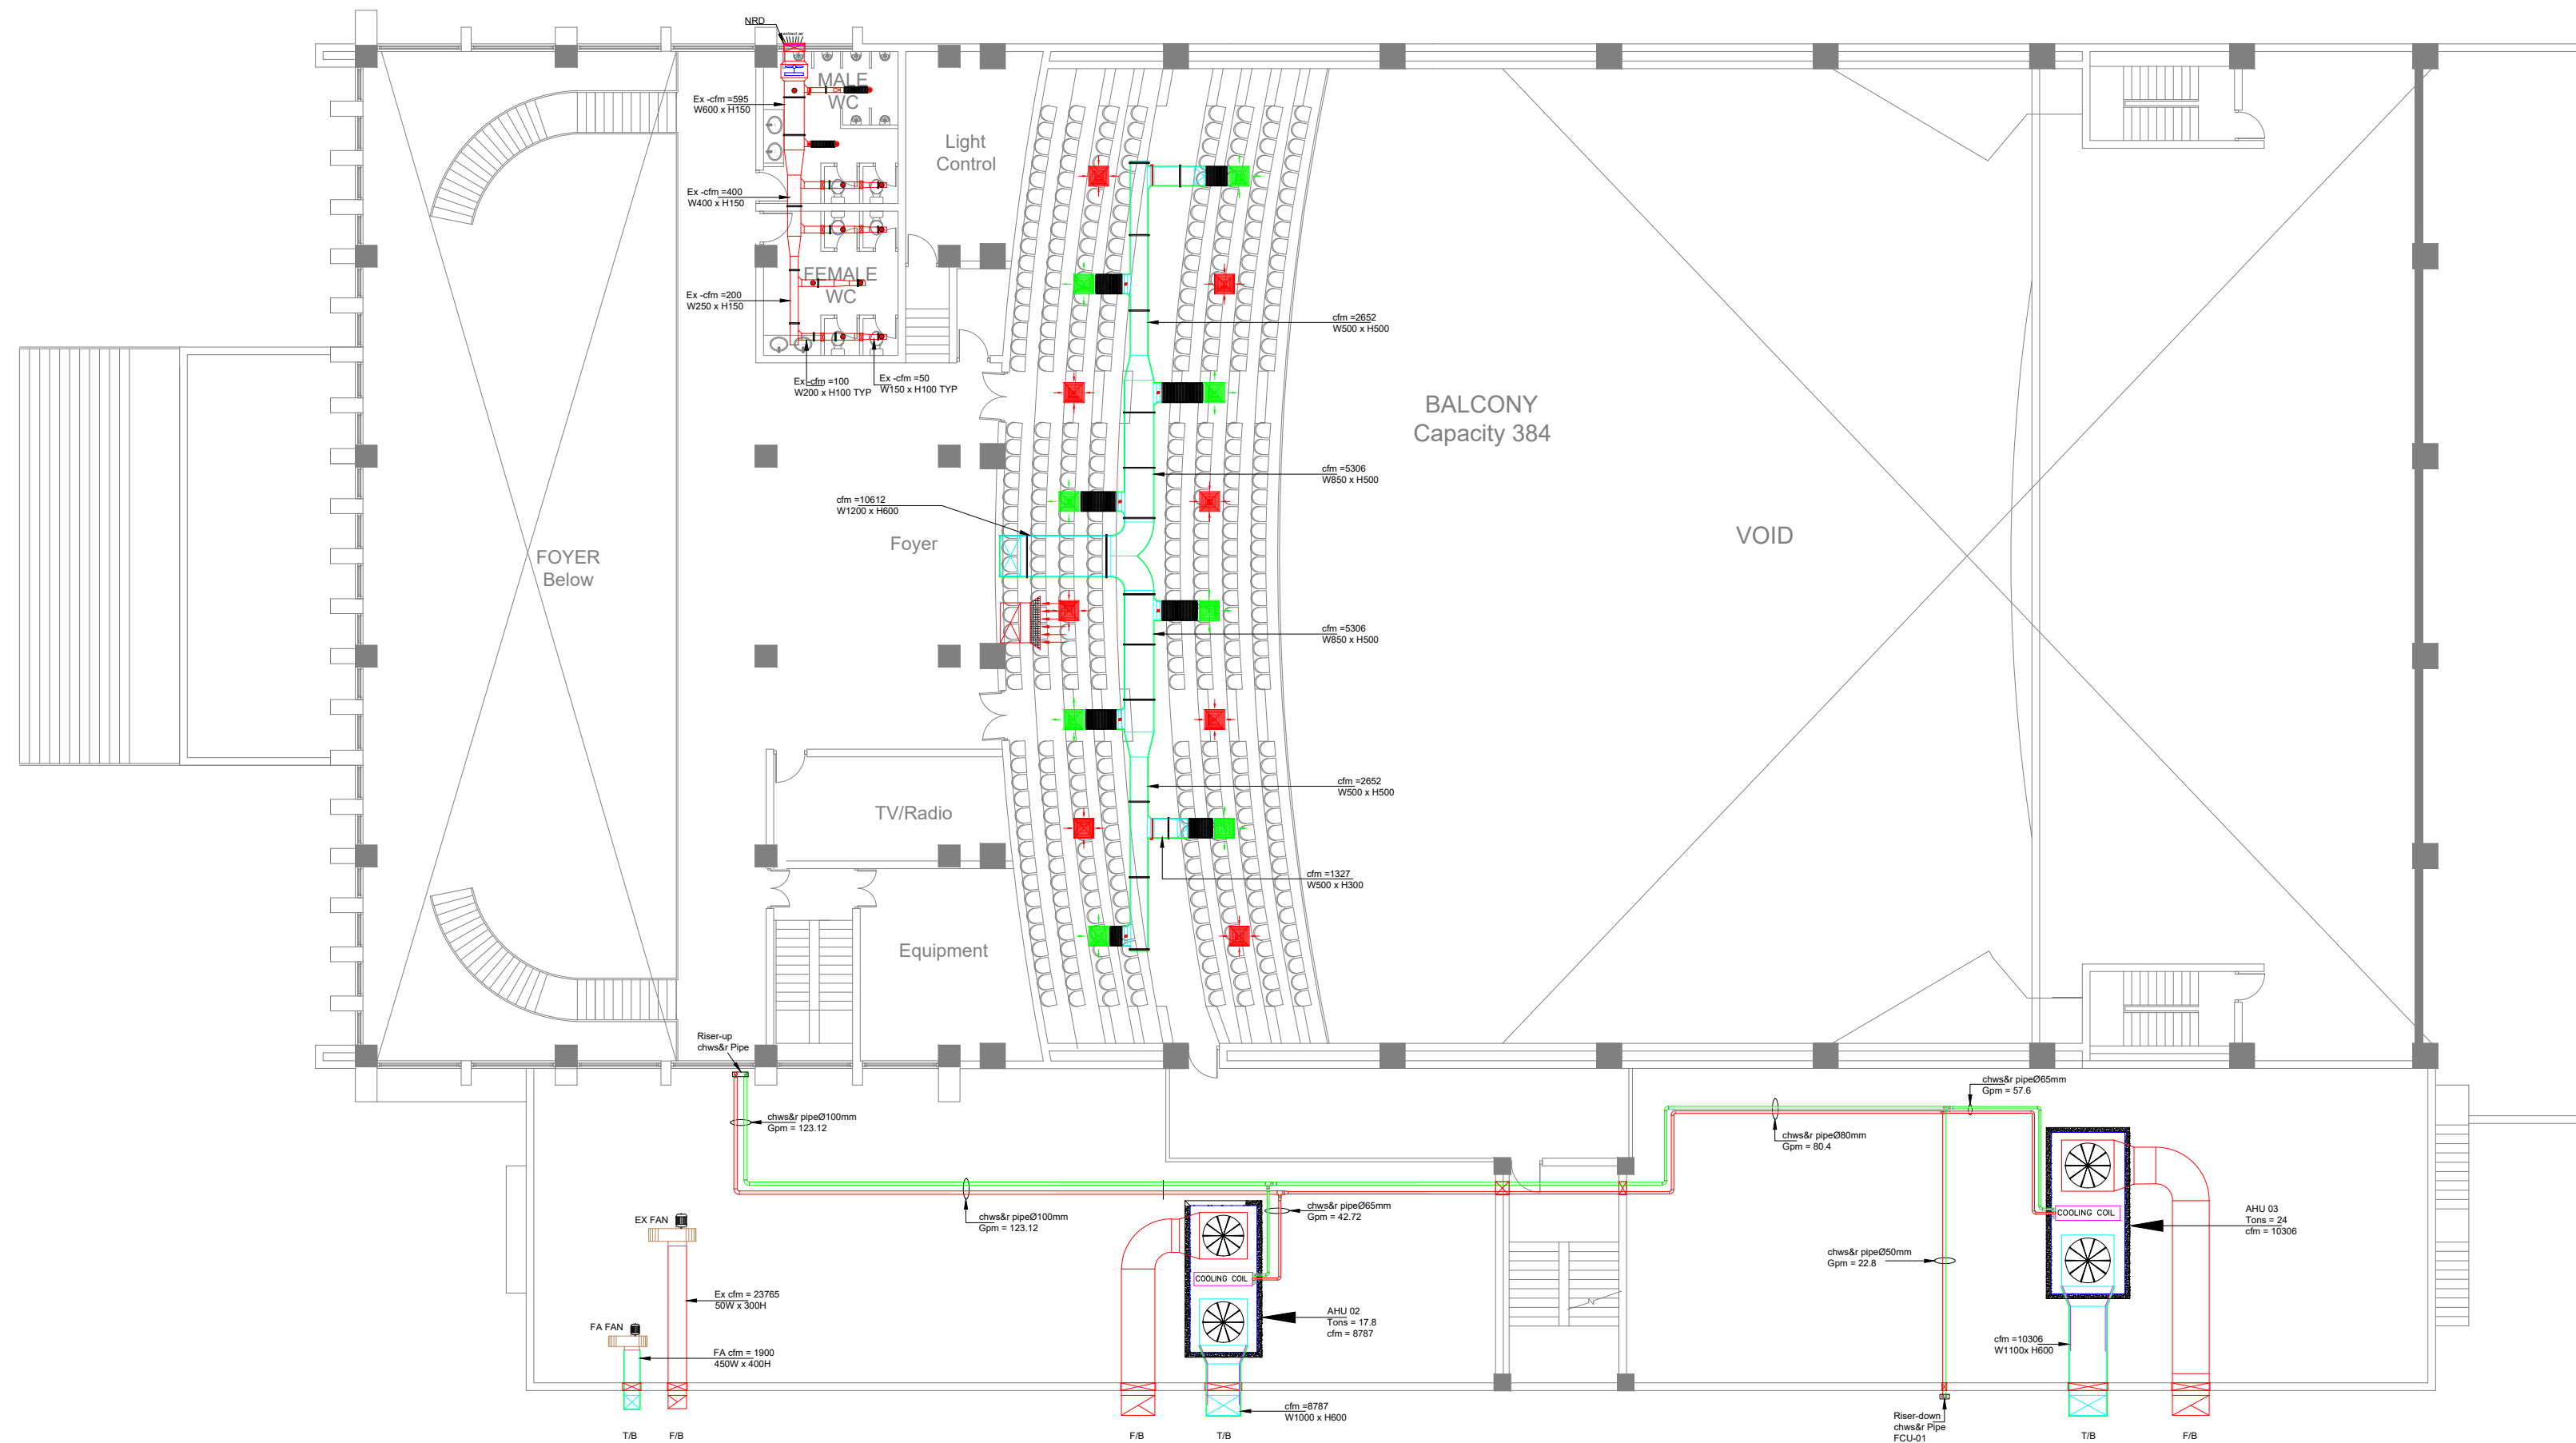

SECOND FLOOR PLAN (lvl.+11000)
Area: 1919 Sq.m
Scale= 1:250

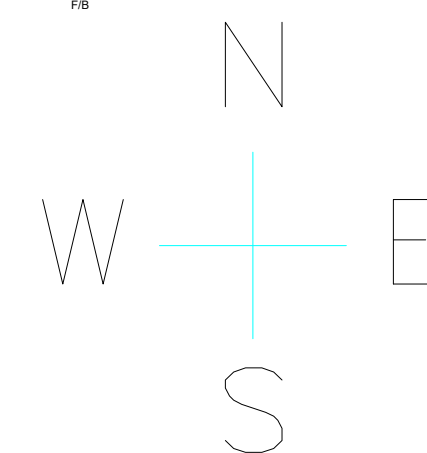

NOTE....
ALL DIMENSION ARE IN MM

SYMBOL	ABBREVIATION
	SUPPLY CEILING DIFFUSER(SCD)
	RETURN CEILING DIFFUSER(RCD)
	WALL OPENING
	FIRE DAMPER
	ACCESS DOOR
	SUPPORTS
	FLEXIBLE DUCT
	THERMOSTAT
	RETURN LINEAR GRILL
	SUPPLY LINEAR GRILL
	VARIABLE AIR VOLUME
	CIRCULAR VOLUME CONTROL DAMPER(VCD)
	INSULATION
	ACCOUSTIC LINING

CLIENT/PROJECT
**AUDITORIUM
INDIA BANGLORE**

**M.E.P.
CONSULTANT**

www.TaibaMEP.Com, tec_mep@yahoo.com, ali@taibamep.com
Ph : 040-64604442 / 9963759411 / 9848461870

Drg. title
**SECOND FLOOR PLAN
HVAC DUCTING LAYOUT**

SCALE	1:100	CHECKED BY ARSLAN A KHAN
DATE	11-12-2019	APPROVED MR. WASIM A K
DRAWN	AZAR PATEL	