


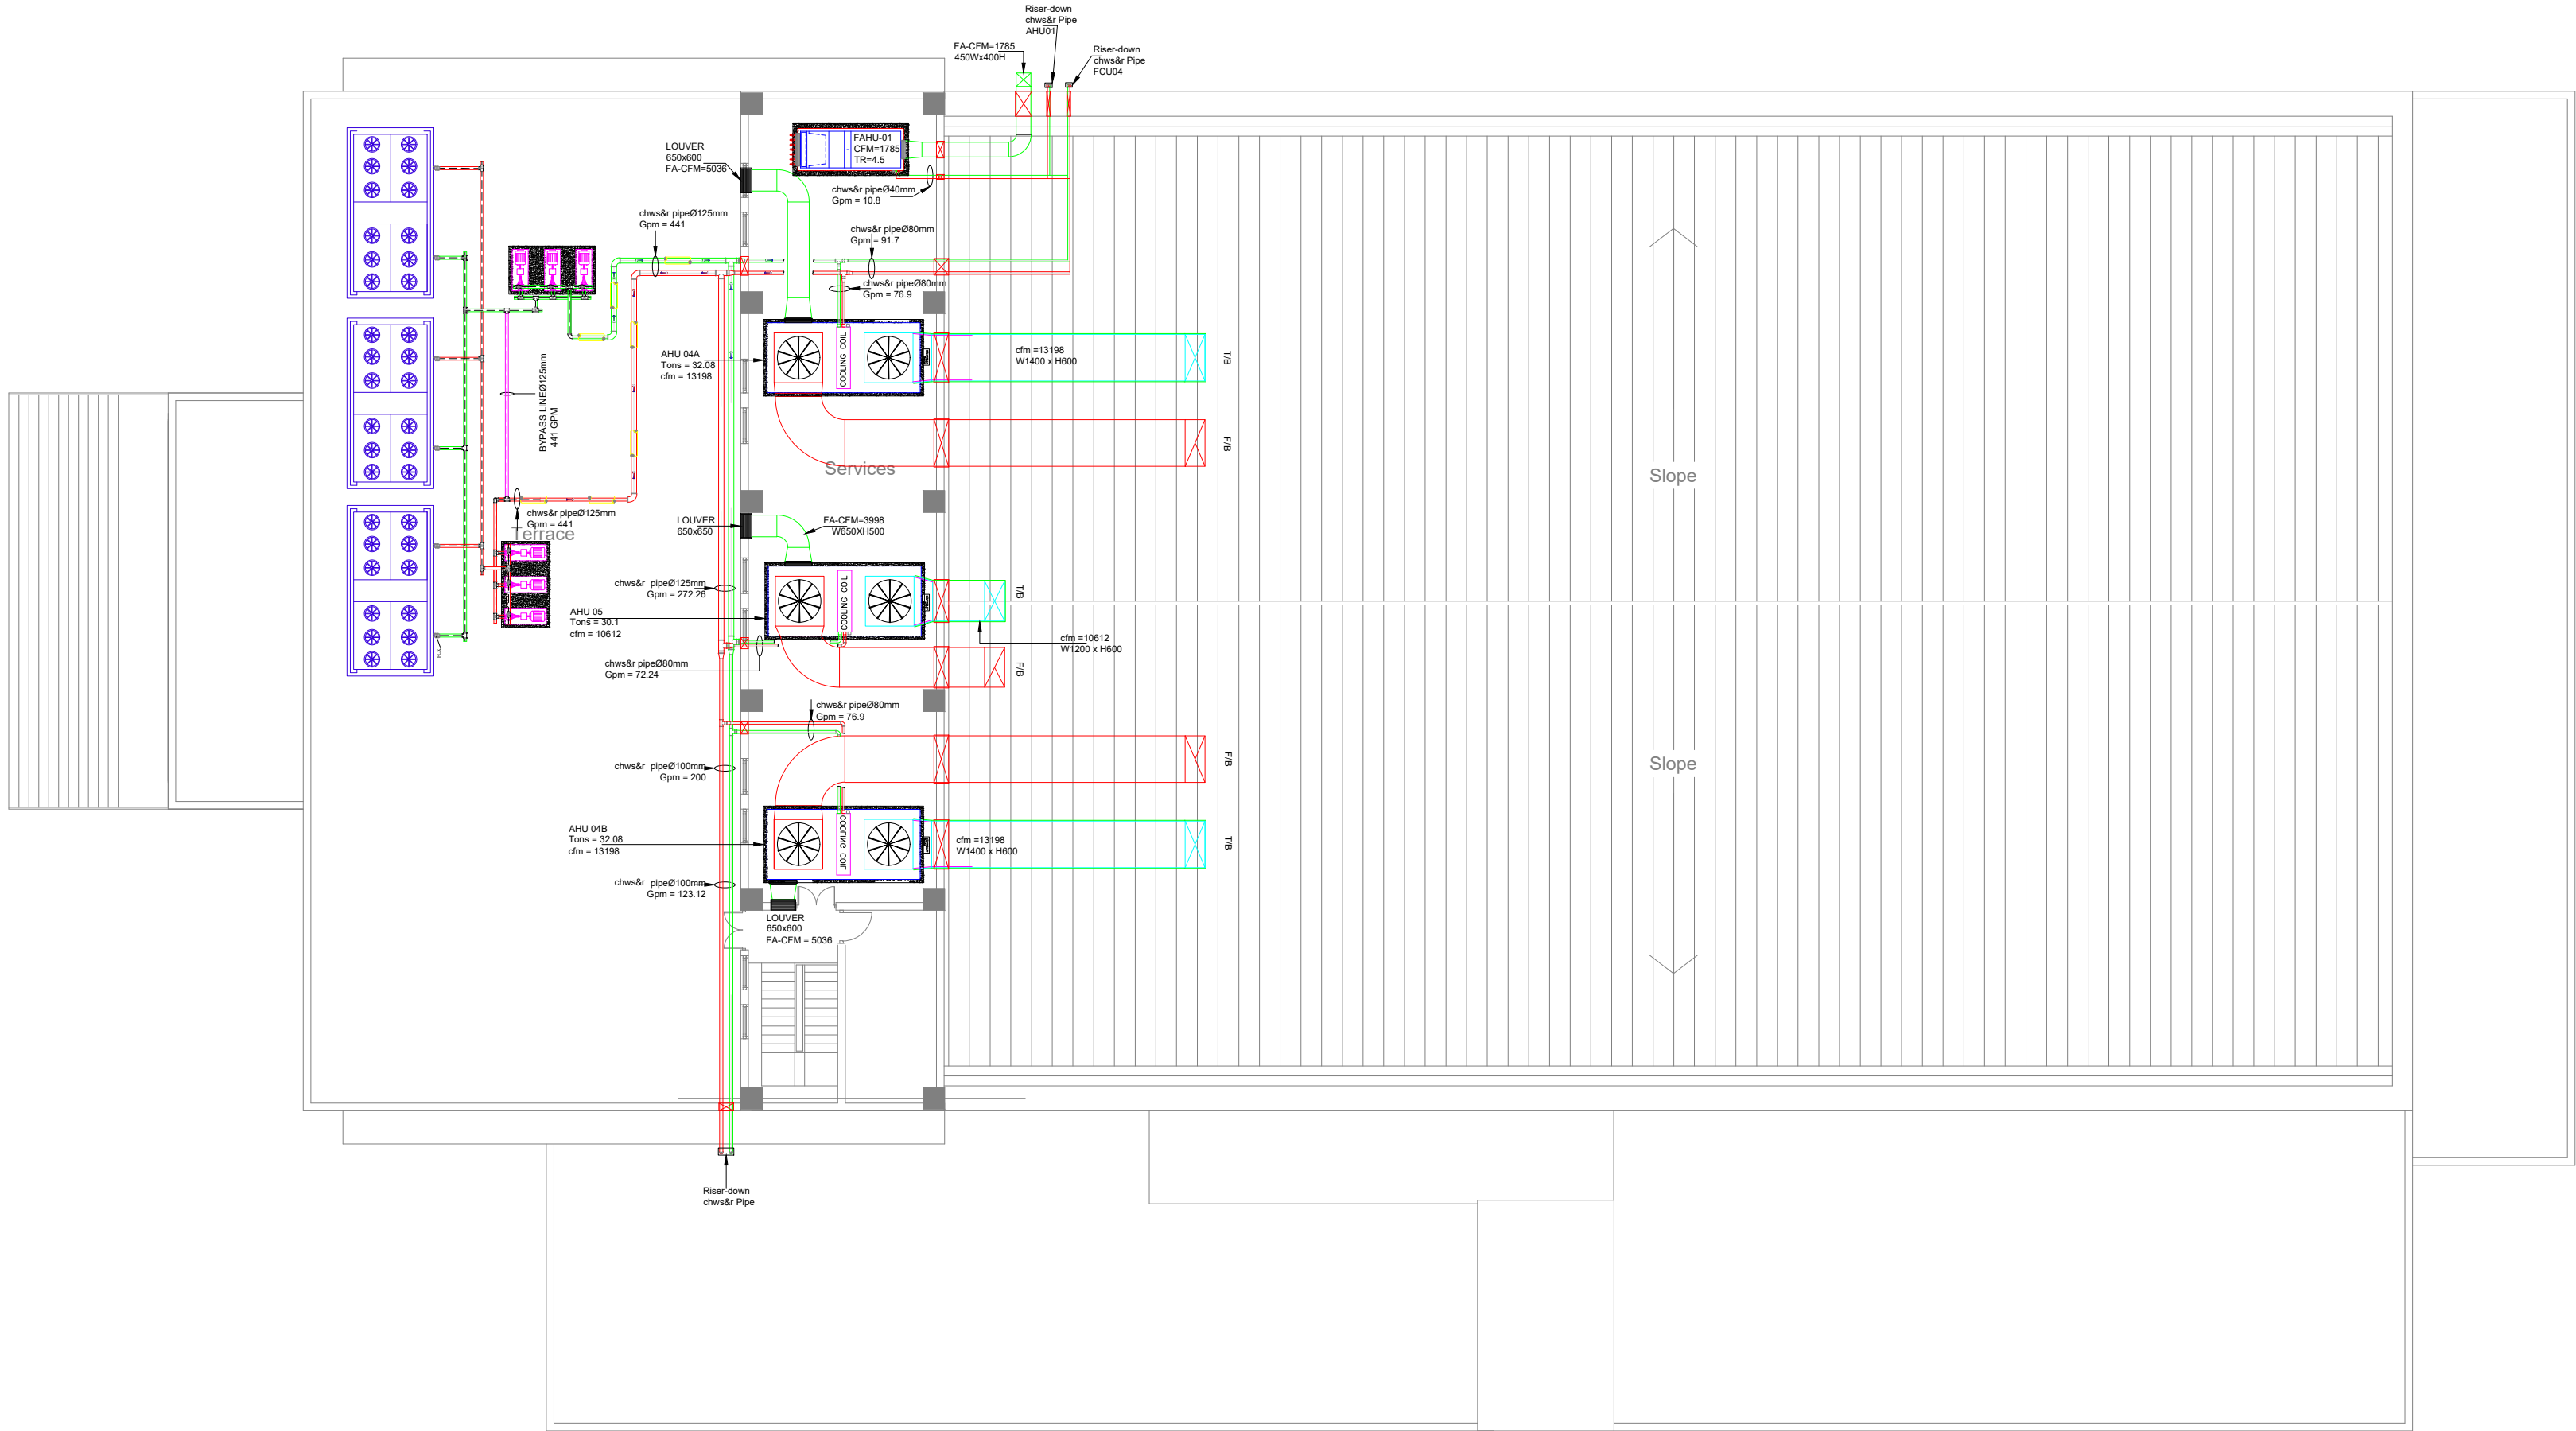

TOP FLOOR PLAN
Area: 203 Sq.m
Scale= 1:250



NOTE....
ALL DIMENSION ARE IN MM

SYMBOL	ABBREVIATION
	INSULATION
	LOUVER
	WALL OPENING
	FIRE DAMPER
	ACCESS DOOR
	SUPPORTS
	FLEXIBLE DUCT
	THERMOSTAT
	RETURN LINEAR GRILL
	SUPPLY LINEAR GRILL
	VARIABLE AIR VOLUME
	CIRCULAR VOLUME CONTROL DAMPER(VCD)
	INSULATION
	ACCOUSTIC LINING

CLIENT/PROJECT
AUDITORIUM
INDIA BANGLORE

M.E.P.
CONSULTANT

www.TaibaMEP.Com, tec_mep@yahoo.com, ali@taibamep.com
Ph : 040-64604442 / 9963759411 / 9848461870

Drg. title
TOP ROOF PLAN
HVAC DUCTING LAYOUT

SCALE	1:100	CHECKED BY ARSLAN A KHAN
DATE	11-12-2019	APPROVED MR. WASIM A K
DRAWN	AZAR PATEL	